DIESE ZEICHNUNG UNTERLIEGT ALS GEISTIGES EIGENTUM DEM URHEBERRECHT
DAS WERKNUTZUNGSRECHT LIEGT BIS AUF AUSDRÜCKLICHEN WIDERRUF BEIM VERFASSER

DIESE ZEICHNUNG UNTERLIEGT ALS GEISTIGES EIGENTUM DEM URHEBERRECHT
DAS WERKNUTZUNGSRECHT LIEGT BIS AUF AUSDRÜCKLICHEN WIDERRUF BEIM VERFASSER

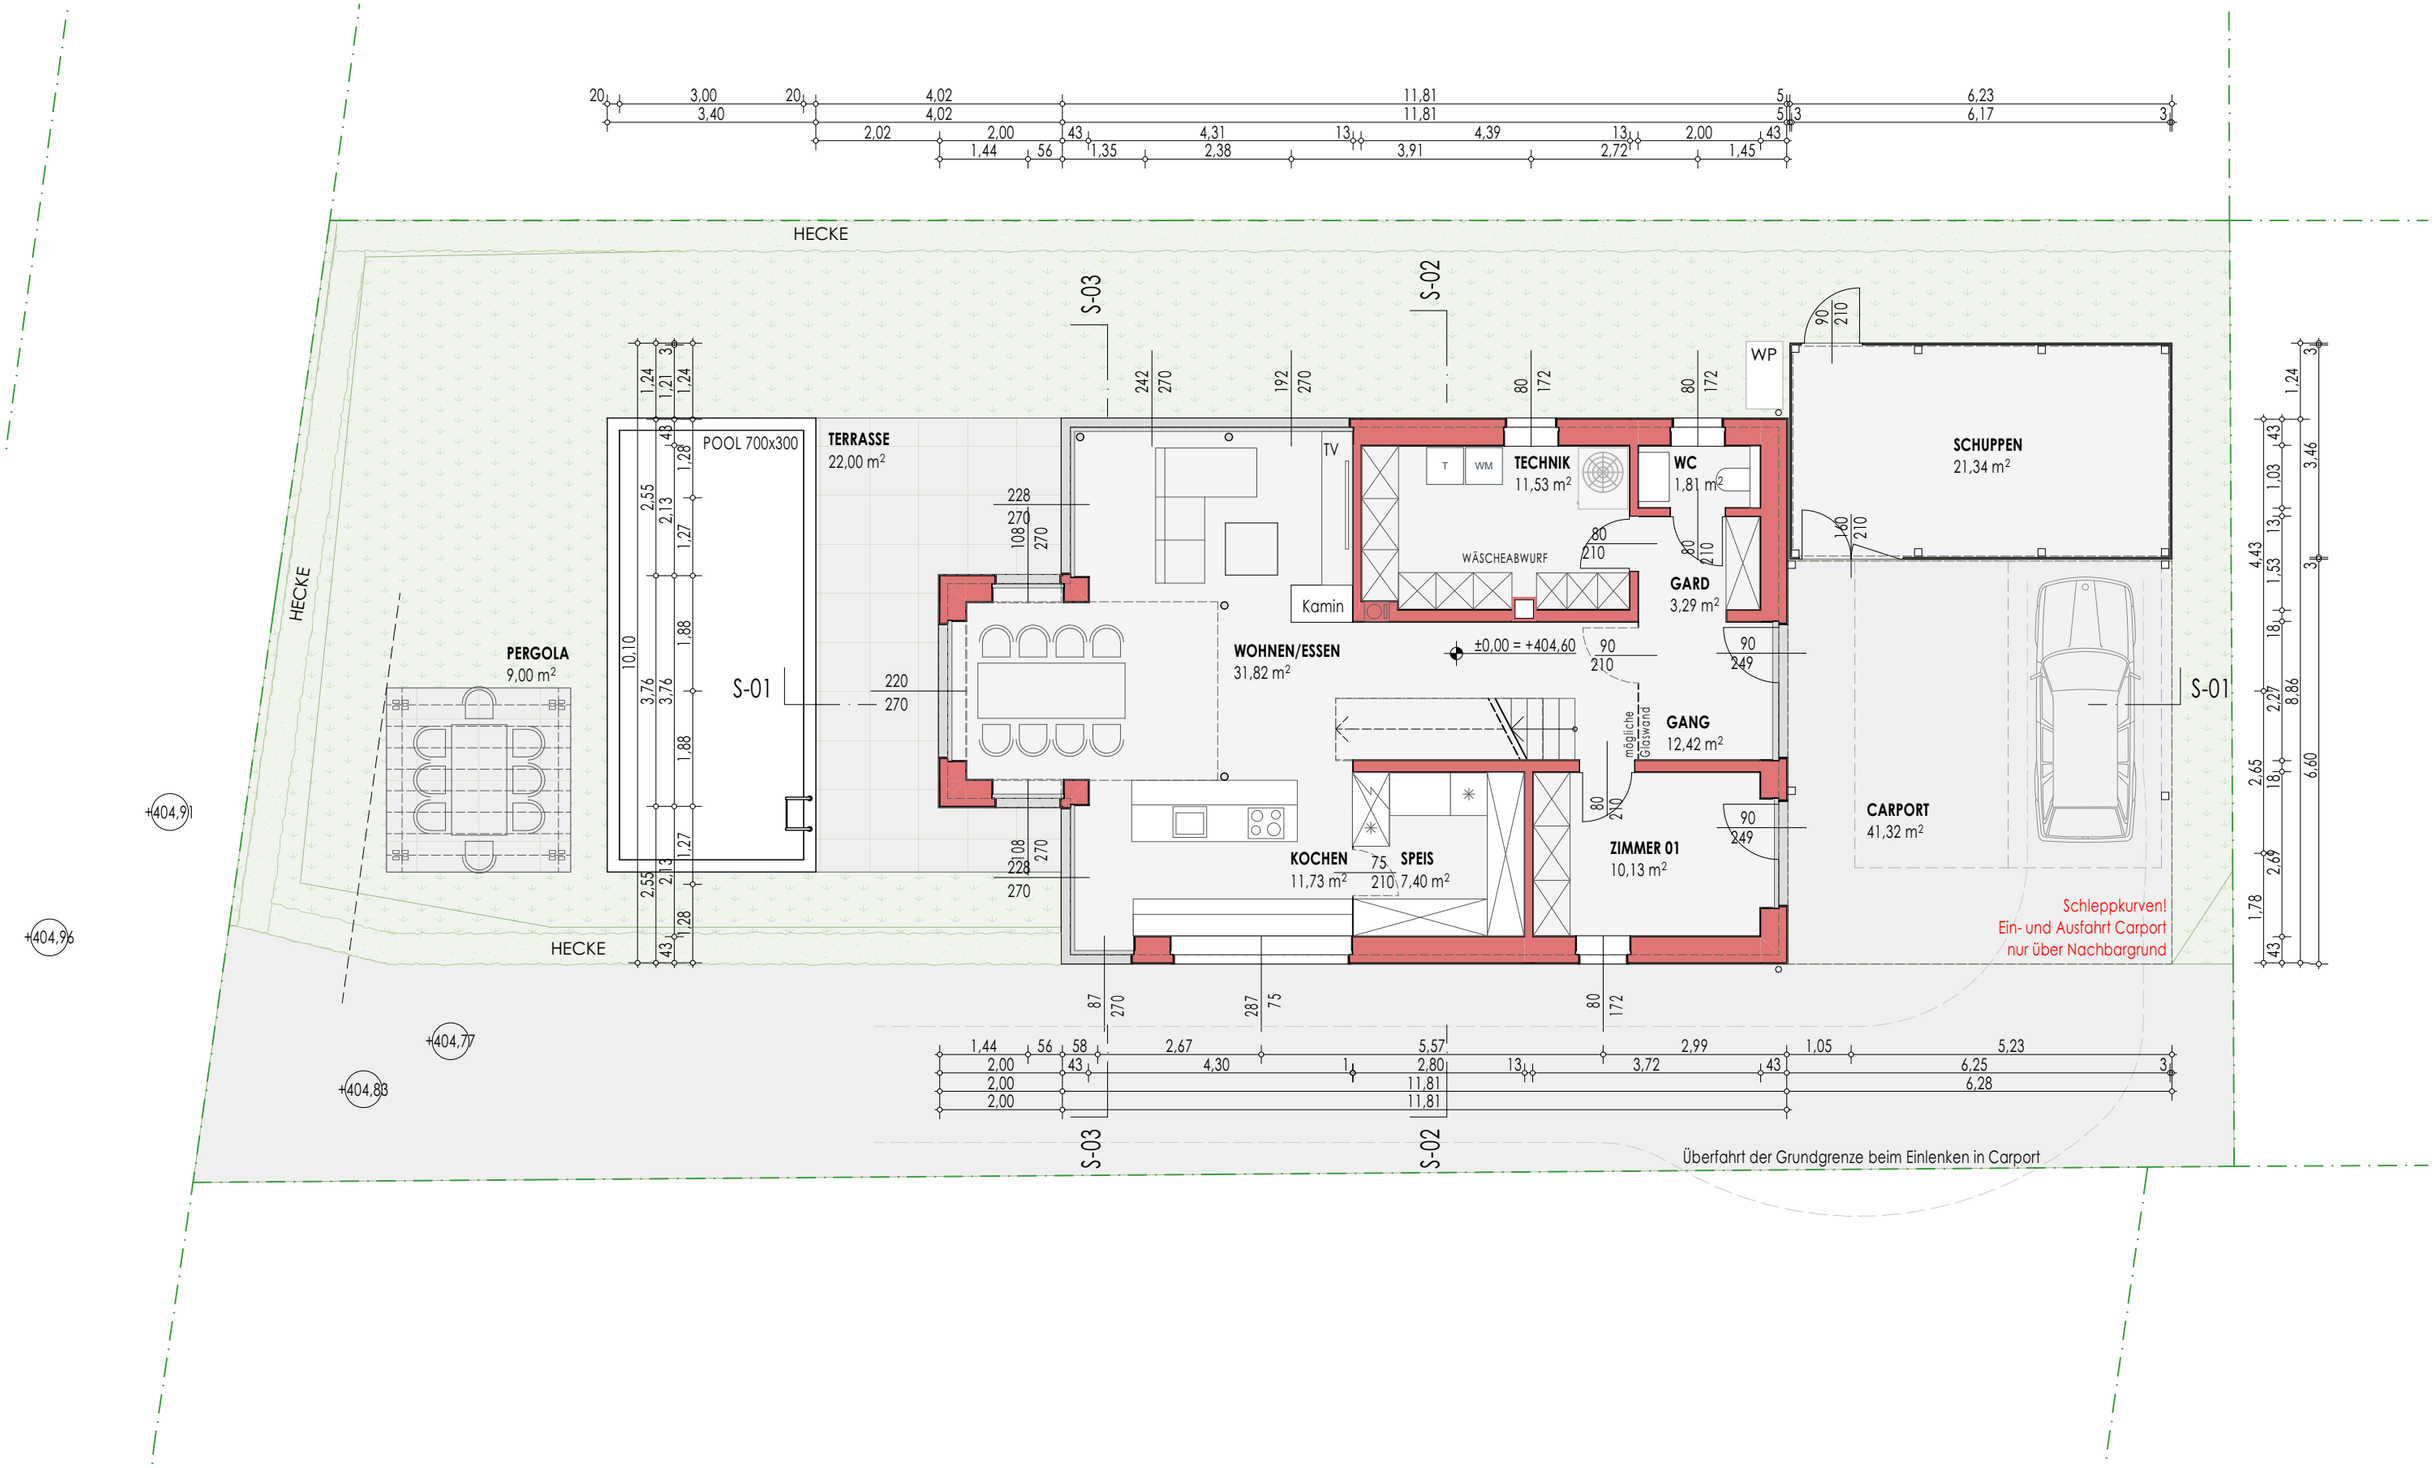

DIESE ZEICHNUNG UNTERLIEGT ALS GEISTIGES EIGENTUM DEM URHEBERRECHT
DAS WERKNUTZUNGSRECHT LIEGT BIS AUF AUSDRÜCKLICHEN WIDERRUF BEIM VERFASSER

	Raum	NNF
Wohnnutzflächen		
EG	GANG	12,42
EG	GARD	3,29
EG	KOCHEN	11,73
EG	SPEIS	7,40
EG	WC	1,81
EG	WOHNEN/ESSEN	31,82
EG	ZIMMER 01	10,13
OG	BAD/WC	8,75
OG	DU/WC	5,33
OG	GANG	8,48
OG	SCHLAFEN	9,74
OG	SCHMINKEN	8,32
OG	SR	6,22
OG	ZIMMER 02	12,28
OG	ZIMMER 03	12,19
		149,91 m²
Nebenflächen		
EG	CARPORT	41,62
EG	SCHUPPEN	21,34
EG	TECHNIK	11,53
		74,49 m²
Befestigte Flächen		
EG	PERGOLA	9,00
EG	TERRASSE	23,54
OG	TERRASSE	41,13

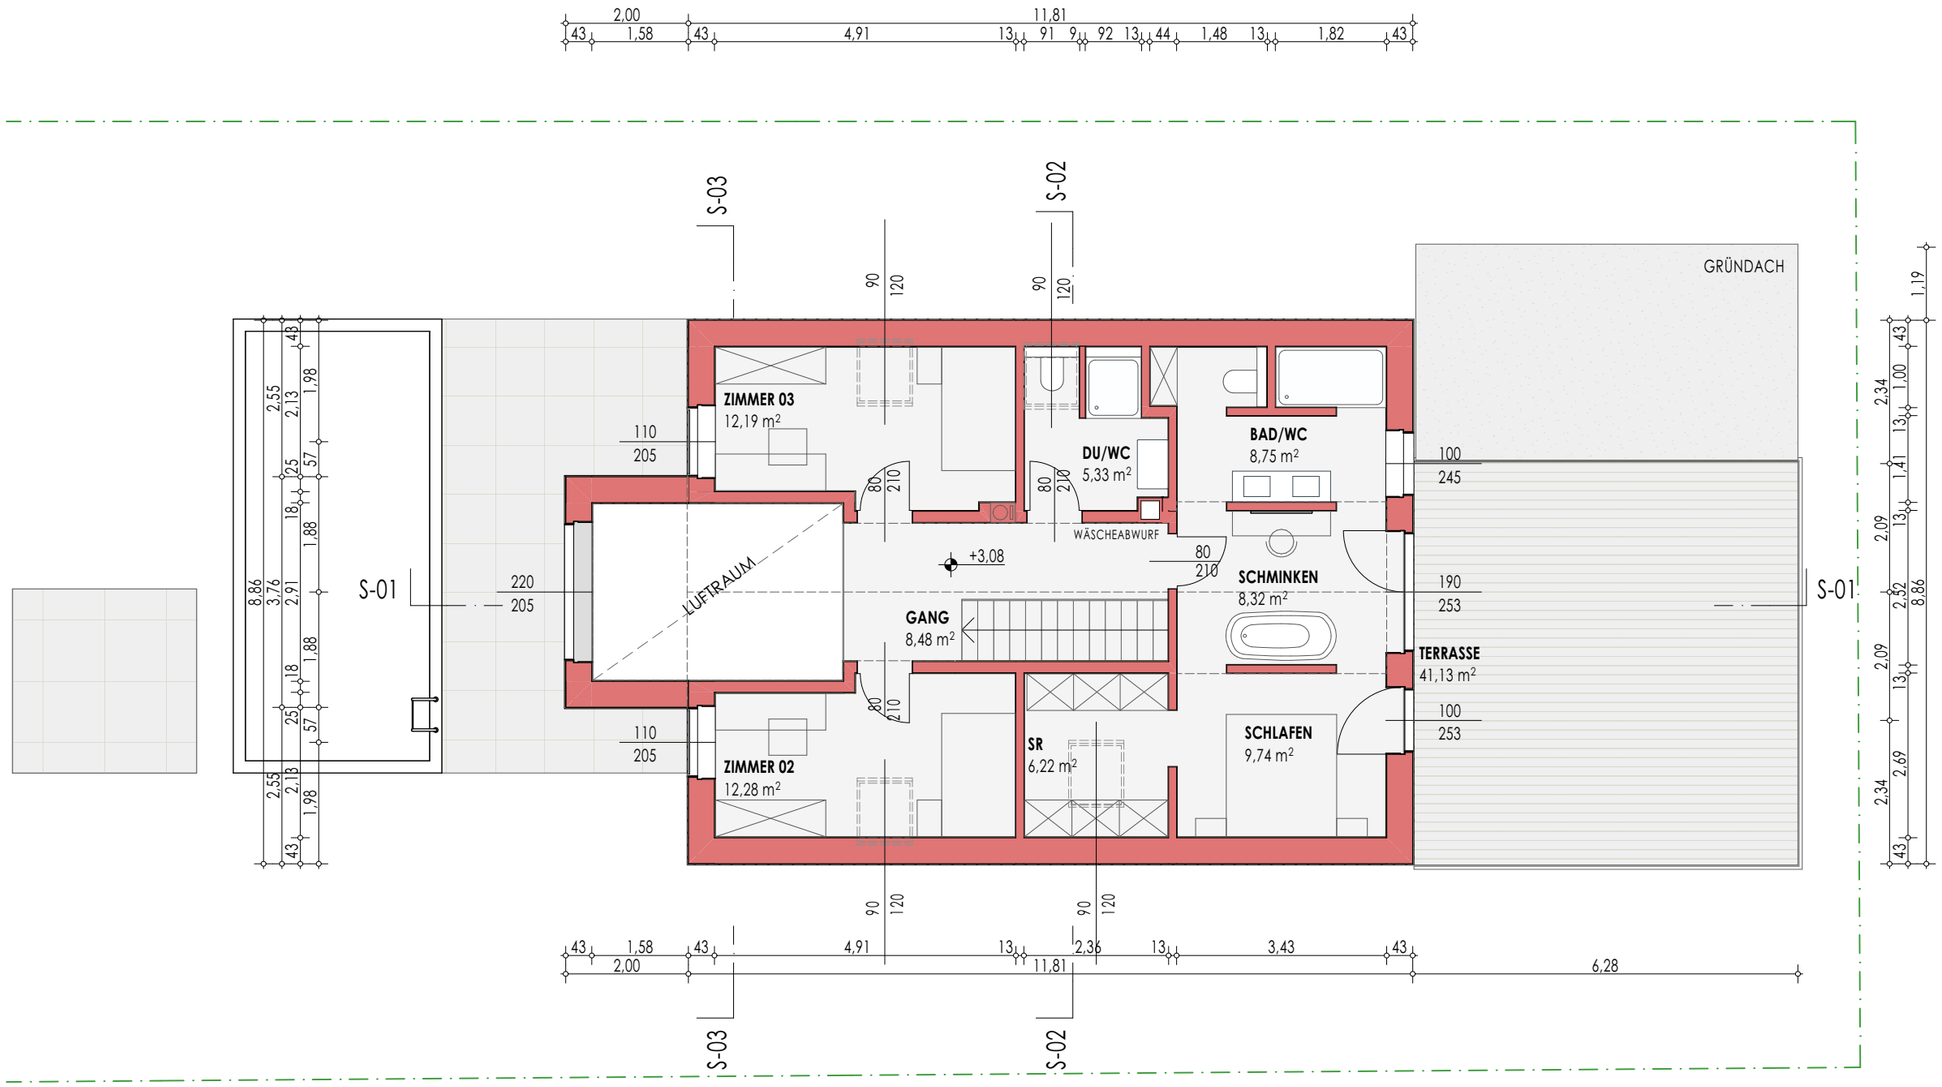

DIESE ZEICHNUNG UNTERLIEGT ALS GEISTIGES EIGENTUM DEM URHEBERRECHT
DAS WERKNUTZUNGSRECHT LIEGT BIS AUF AUSDRÜCKLICHEN WIDERRUF BEIM VERFASSER

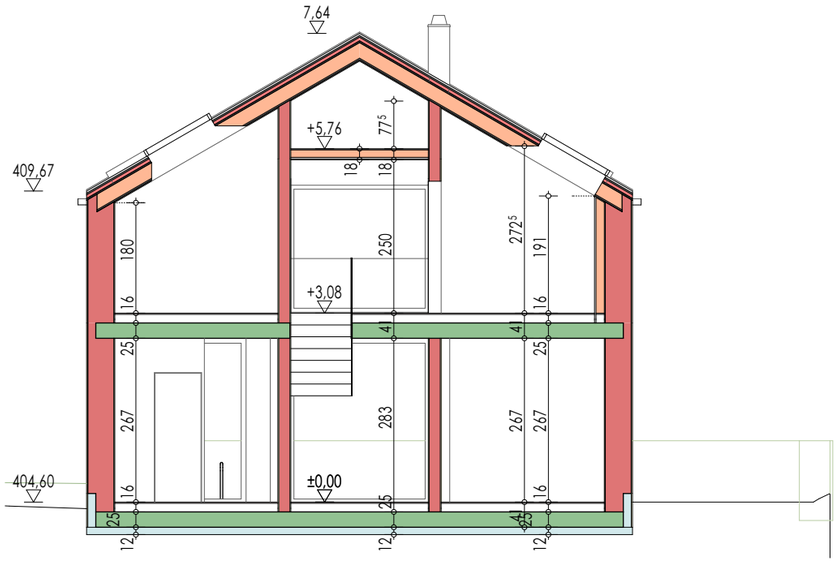

SCHNITT 02 M 1:100

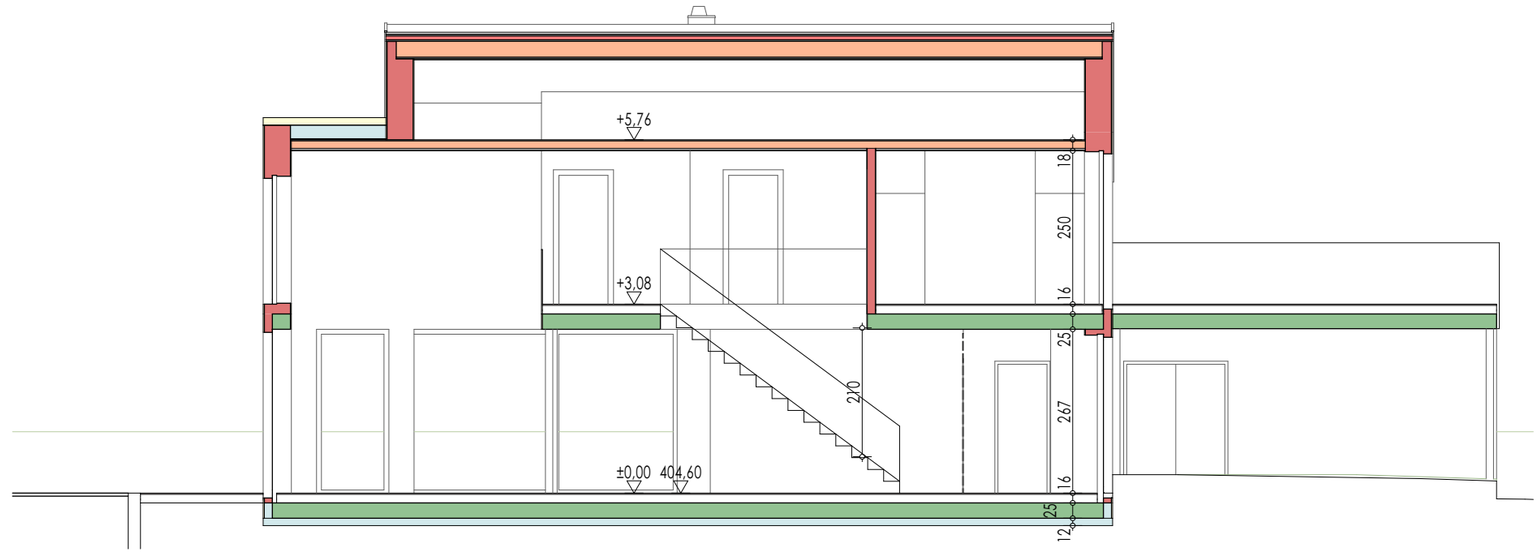

SCHNITT 01 M 1:100

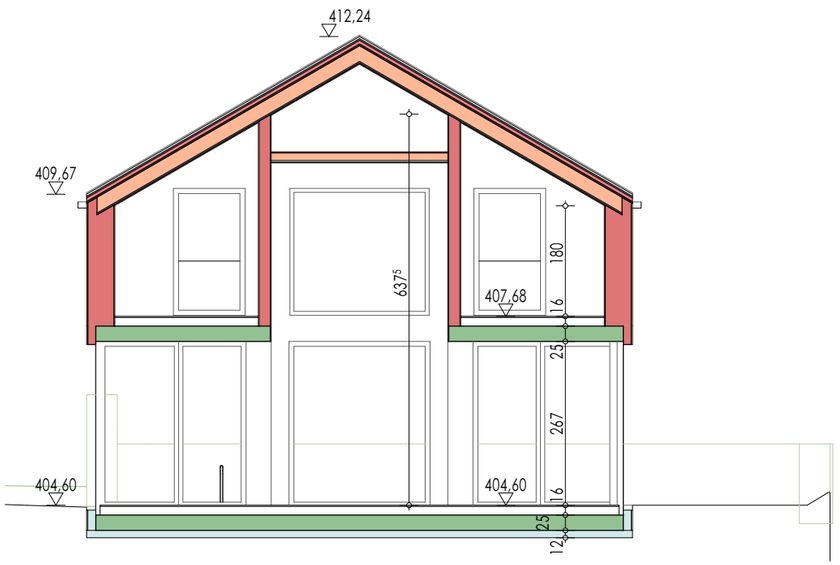

SCHNITT 03 M 1:100

DIESE ZEICHNUNG UNTERLIEGT ALS GEISTIGES EIGENTUM DEM URHEBERRECHT
DAS WERKNUTZUNGSRECHT LIEGT BIS AUF AUSDRÜCKLICHEN WIDERRUF BEIM VERFASSER

ANSICHT OST M 1:100

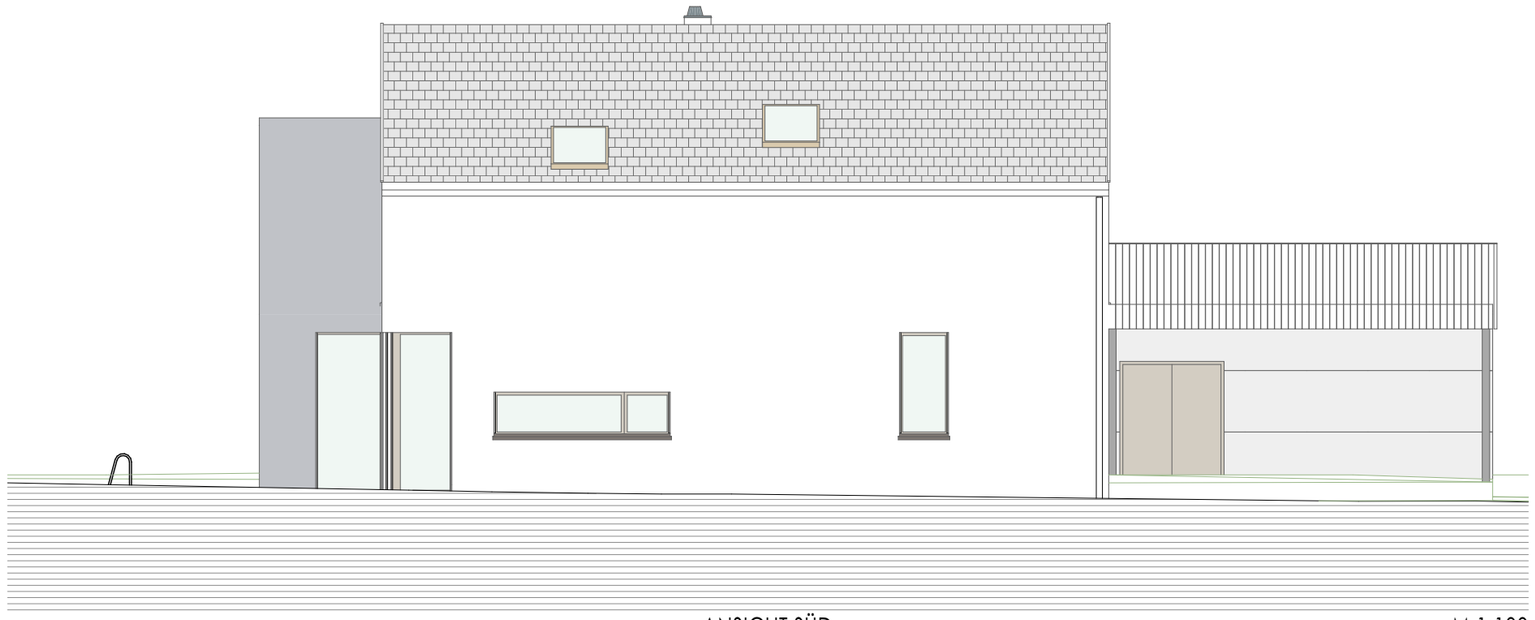

ANSICHT SÜD M 1:100

DIESE ZEICHNUNG UNTERLIEGT ALS GEISTIGES EIGENTUM DEM URHEBERRECHT
DAS WERKNUTZUNGSRECHT LIEGT BIS AUF AUSDRÜCKLICHEN WIDERRUF BEIM VERFASSER

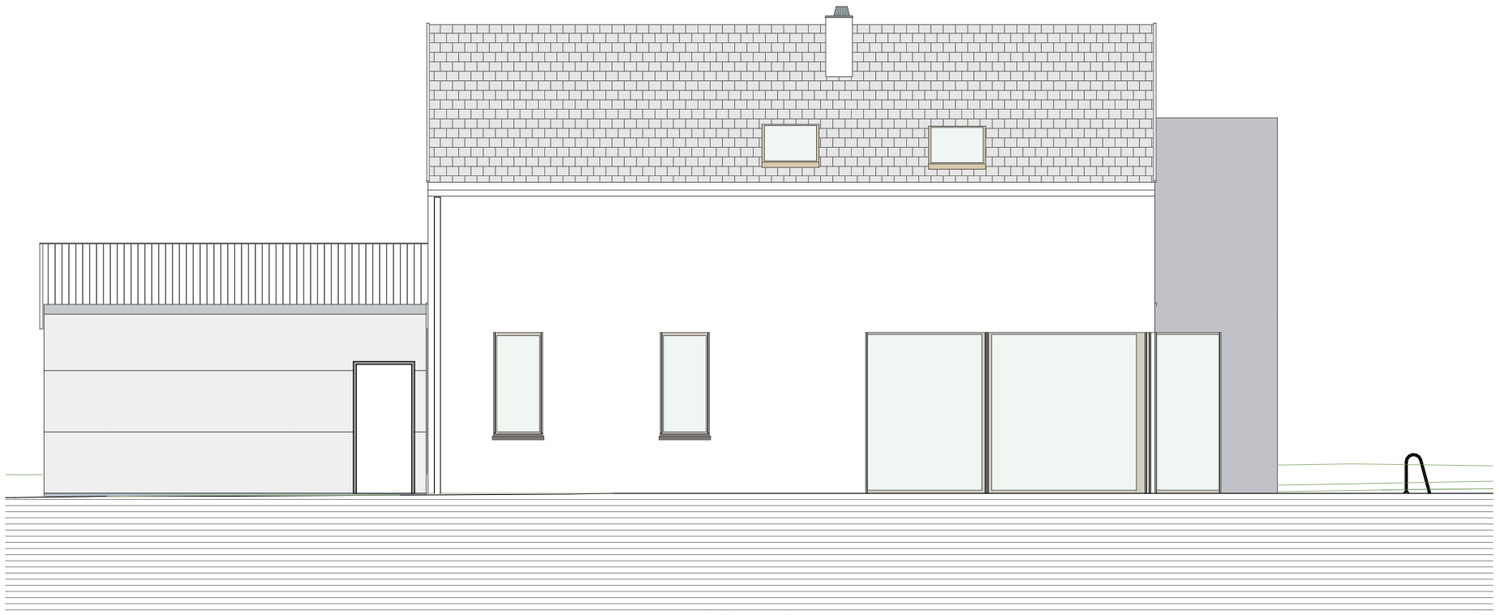

ANSICHT NORD M 1:100

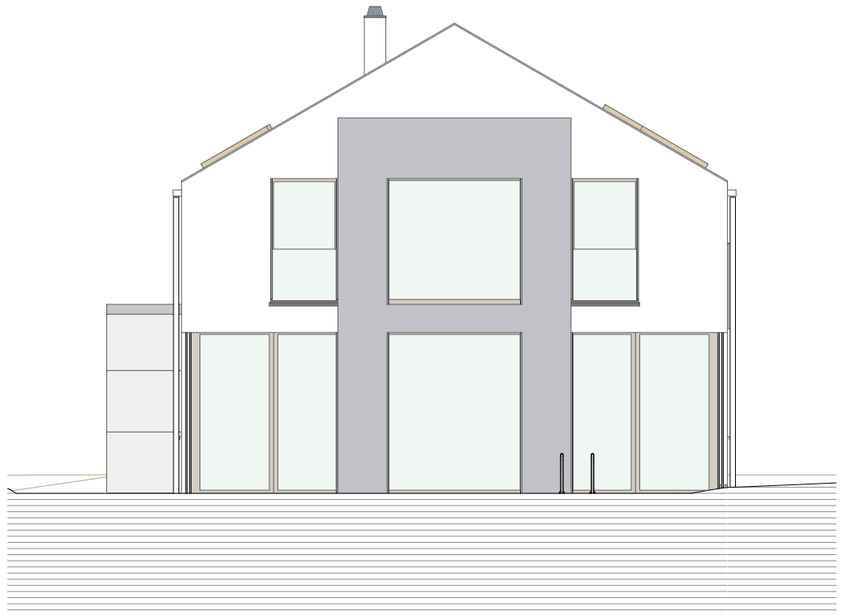

ANSICHT WEST M 1:100

DIESE ZEICHNUNG UNTERLIEGT ALS GEISTIGES EIGENTUM DEM URHEBERRECHT
DAS WERKNUTZUNGSRECHT LIEGT BIS AUF AUSDRÜCKLICHEN WIDERRUF BEIM VERFASSER